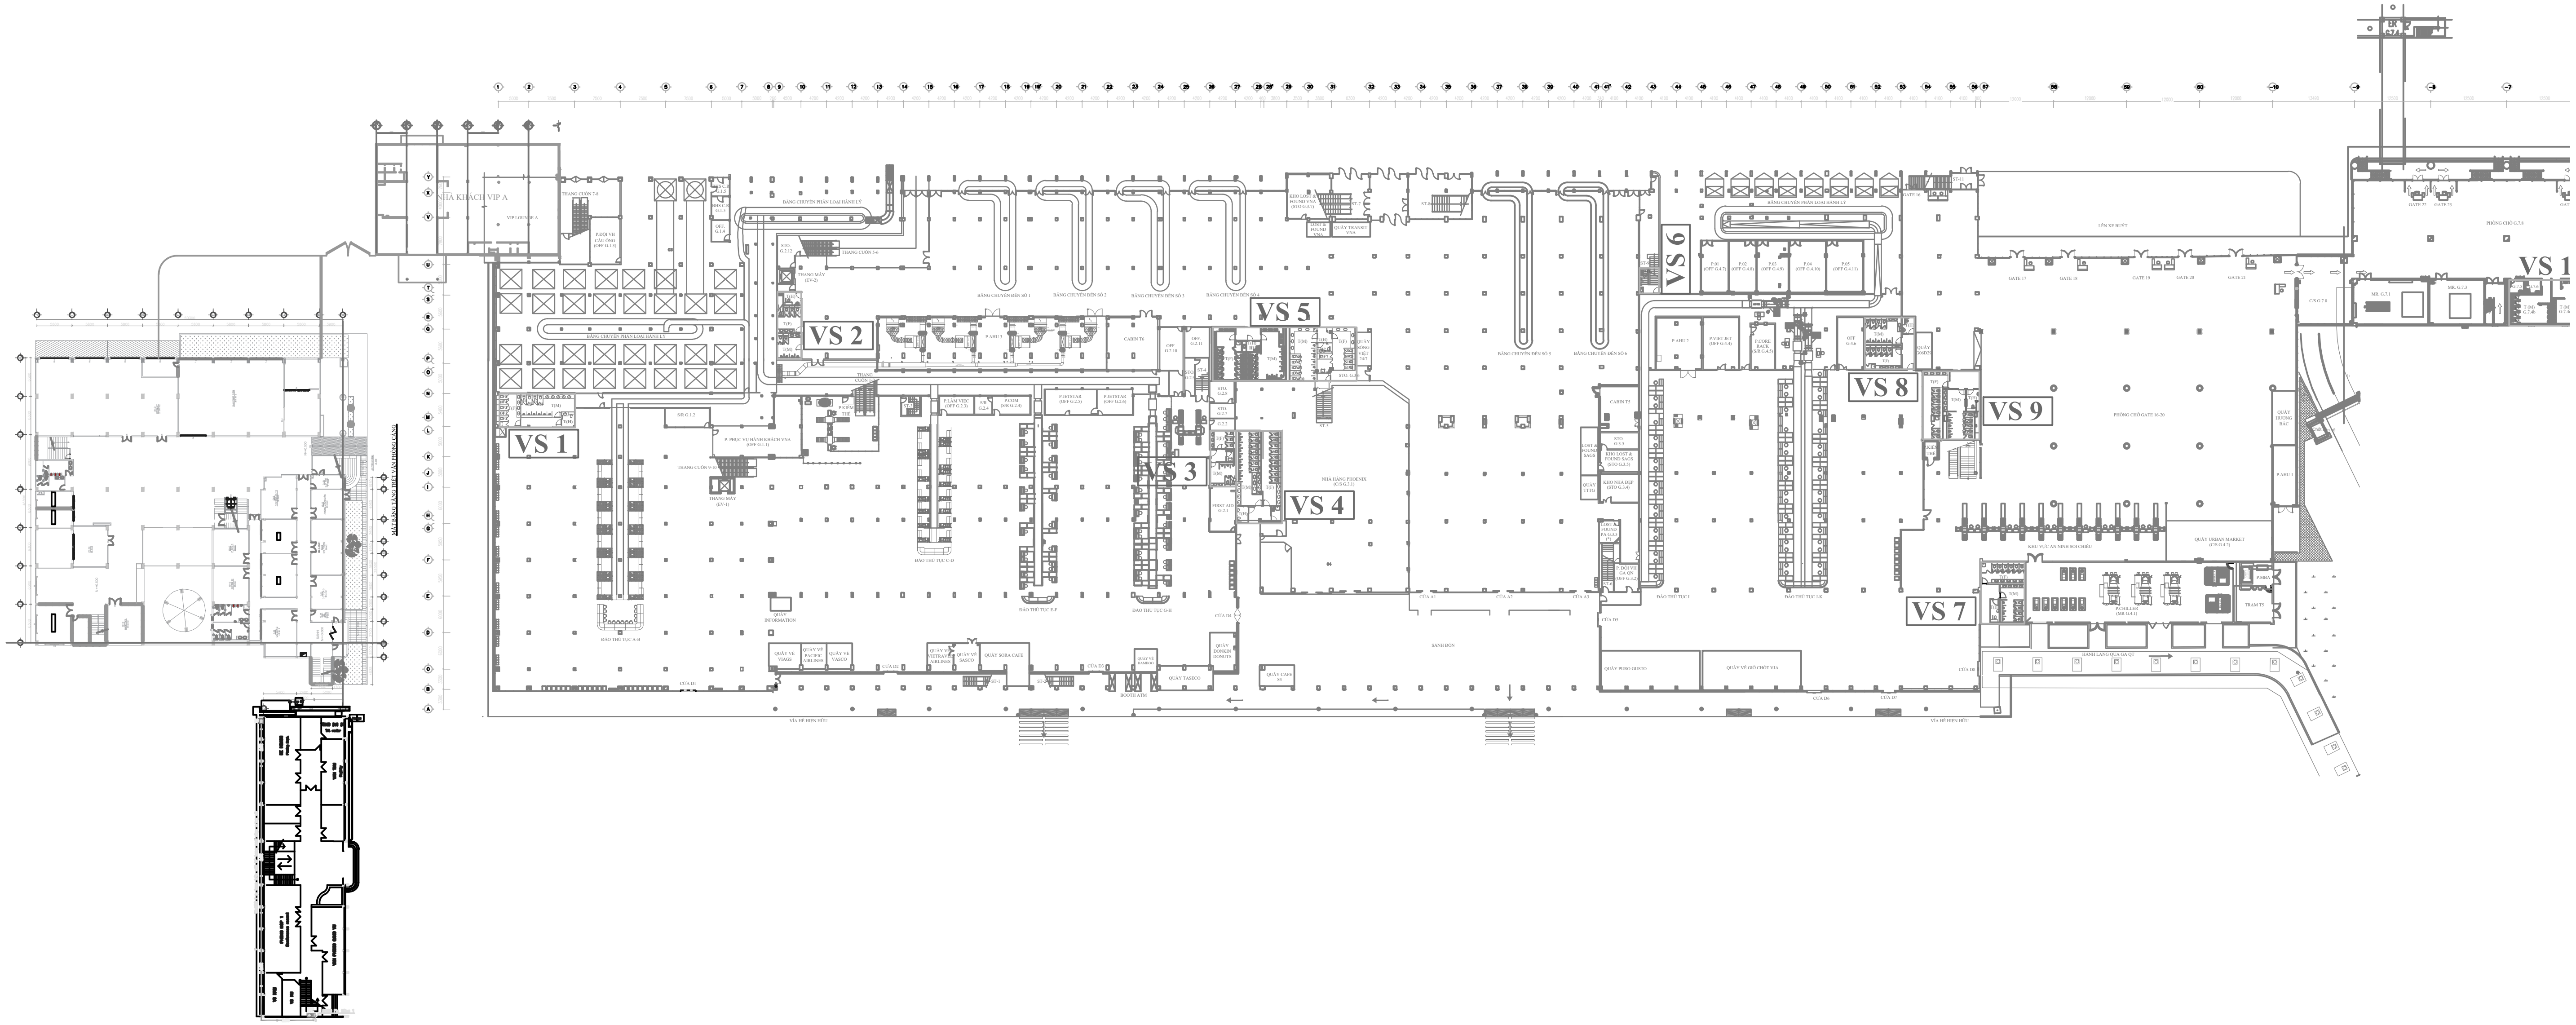
NHÀ KHÁCH VIP A
VS 1
VS 2
VS 3
VS 4
VS 5
VS 6
VS 7
VS 8
VS 9
VS 1